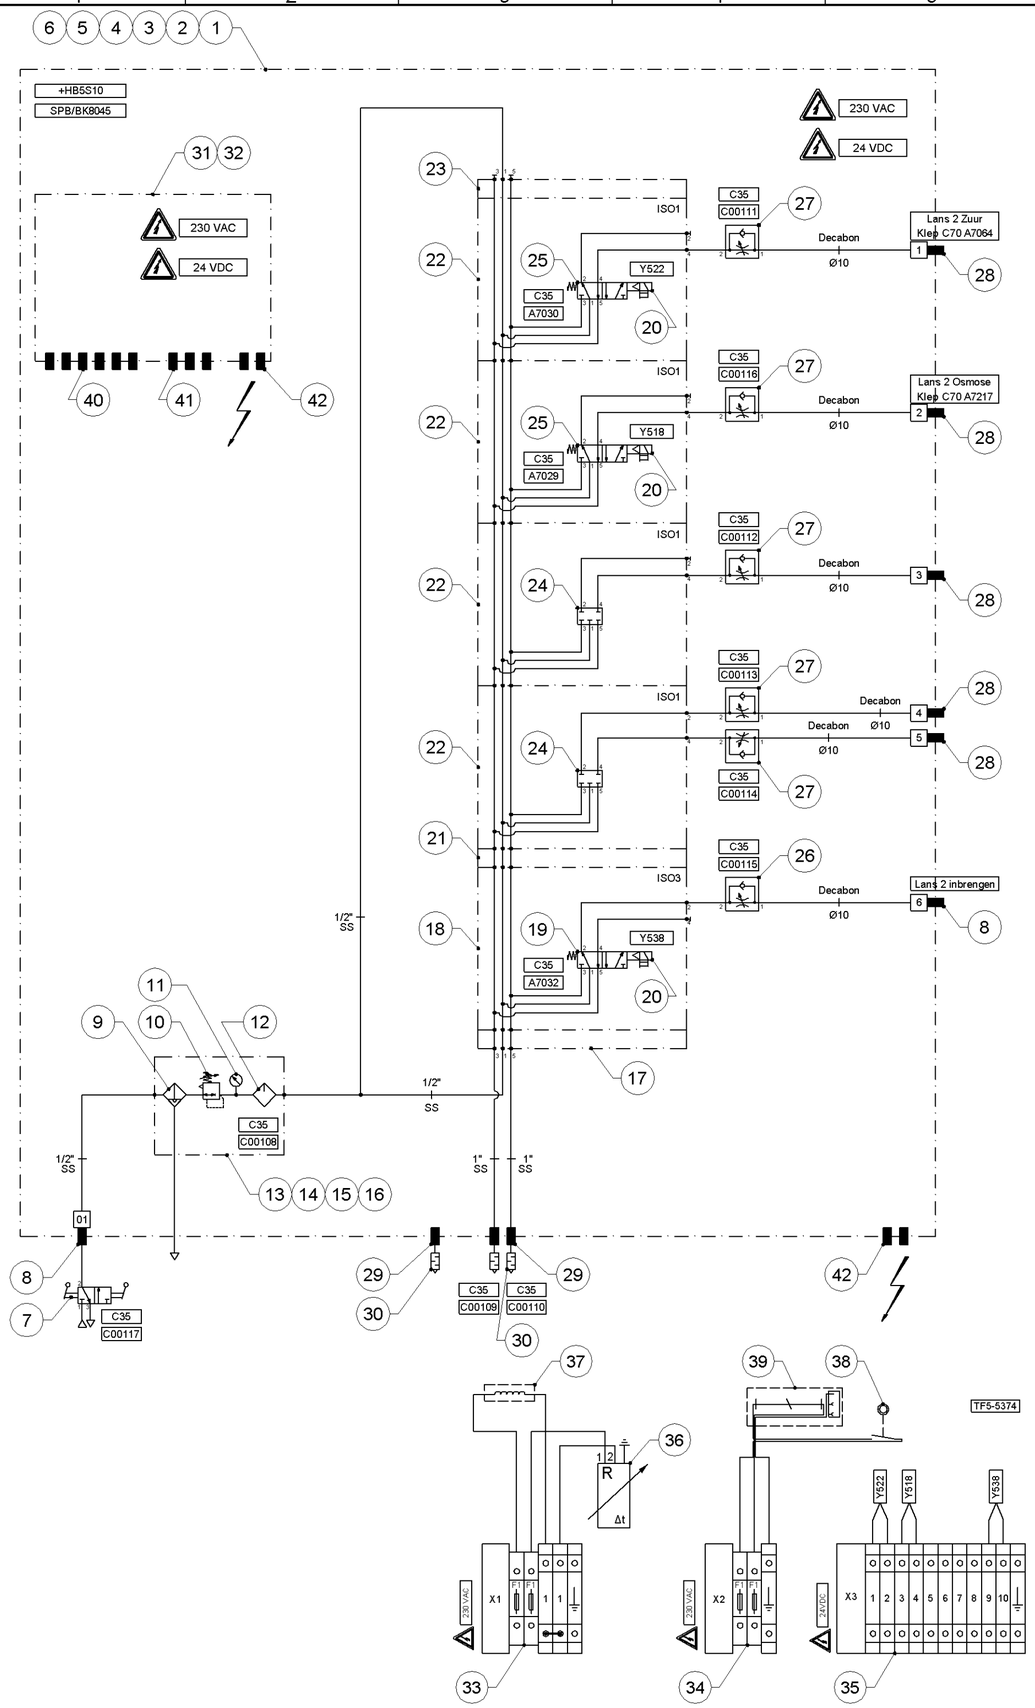

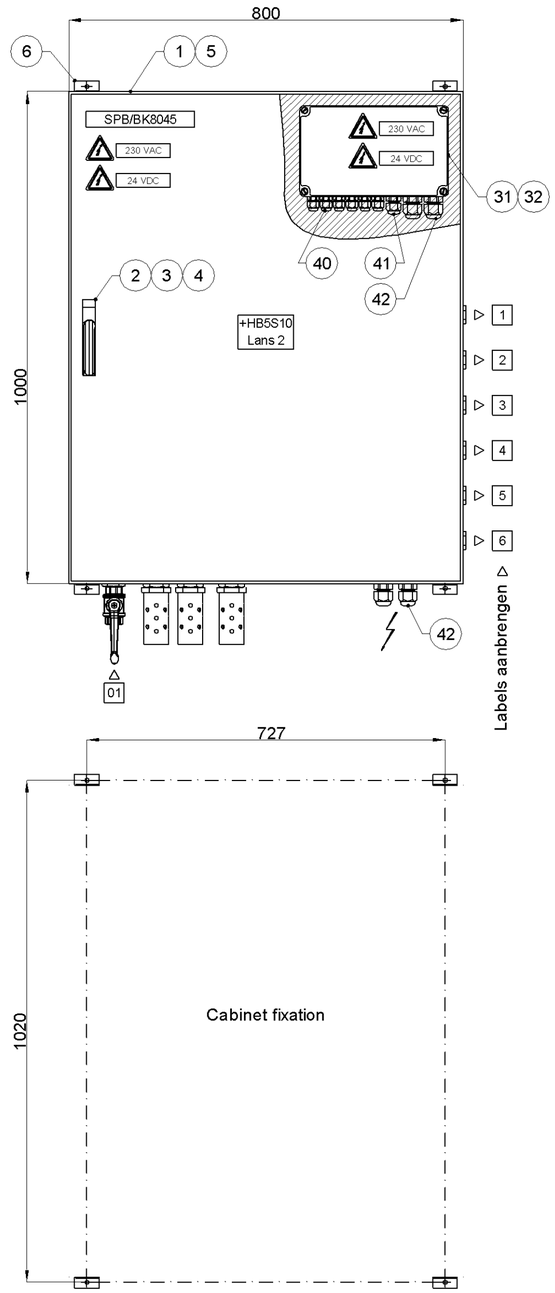

Pos.	Qty.	Type	Con.	Description
42	4	PGM25-9-17		Kabelwartel M25 (9.0-17.0mm)
41	3	PGM20-6-13		Kabelwartel M20 (6.0-13.0mm)
40	6	PGM16-4,5-10		Kabelwartel M16 (4.5-10.0mm)
39	1	21415/6308		TL-lamp
38	1	21474/6308		Deurschakelaar
37	1	17515/6308		Verwarmingselement 150W
36	1	17561/6308		Thermostaat
35	1	LPB/TERMINALS-WEIDMUL-ASS		Klemmenstrook Weidmüller
34	1	LPB/5SY6102-7		Automaat 2P 2A
33	1	LPB/5SY6204-7		Automaat 2P 4A
32	1	LPB/856112		Scharnieren voor APO kast
31	1	LPB/856058		Polyester kastje 300x185x175
30	3	MB008B	1"	Gepantserde geluiddemper 1"
29	3	M911INOX	1"	Schotdoorvoerkopp. RVS G1
28	5	M911/4INOX	1/4"	Schotdoorvoerkopp. RVS G1/4
27	5	T1000C2800	1/4"	Snelheidsregelventiel G1/4
26	1	T1000C4800	1/2"	Snelheidsregelventiel G1/2
25	2	SXE9573-Z71-81-33N		5/2 el.pneum.ventiel veer ISO1 24VDC
24	1	CQM/22152/3/23		Blindplaat
23	1	CQM/22152/3/22	1/4"	Stel eindplaten ISO1
22	4	CQM/22152/3/21		Rijgbare basisplaat ISO1 onderkant
21	1	CQM/22354/3/32		Verloopplaat ISO3 naar ISO1
20	3	M/P43316/13		30mm steker Led 12-24V + Kabel 3m
19	1	SXE9575-Z71-81-33N		5/2 el.pneum.ventiel veer ISO3 24VDC
18	1	CQM/22354/3/21		Rijgbare basisplaat ISO3 onderkant
17	1	CQM/22354/3/22	1/2"	Stel eindplaten ISO3
16	1	74504-50		Wandbevestiging
15	1	74503-51		Koppelstuk voor frames
14	1	Y64A-4GA-N1N	1/2"	Frame dubbele uitv. G1/2
13	1	Y64A-4GA-N2N	1/2"	Frame dubbele uitv. G1/2
12	1	L64M-NNP-EDN		Smeertoestel Micro-Fog
11	1	18-013-013	1/8"	Mano Ø50 rugaansl. R1/8 0-10 bar
10	1	R64G-NNK-RMN		Reduceerventiel R. 10 bar
9	1	F64G-NNN-AD3		Filter 40µ. auto. metalen res.
8	2	M911/2INOX	1/2"	Schotdoorvoerkopp. RVS G1/2
7	1	602113148EX	1/2"	3/2 afsluitkraan G1/2
6	1	KS1483.000/1040		Wandbevestiging kast
5	1	SZ2514.000		Rittal Tekeninghouder A4
4	1	SZ2546.000		Driehoeksleutel 8mm Rittal
3	1	SZ2463.000		Rittal kast insert driekantslot 8mm
2	1	KS1490.000/1040		Vergrend. ergoform voor KS1468
1	1	KS1480/1040		Polyester kast 1000x800x300

Type Plan:

Voor samenstelling zie: SPB/BK8045

Index	Datum	Beschrijving	TWA	Naam	Nagezien
	16/06/2017	EERSTE UITGAVE			

Studie gemaakt door: M.Marchant

	Naam:	Datum:
Getekend:	N.Bredoux	05/10/16
Nagezien:	M.Marchant	06/10/16

Schaal: N.A.
Formaat: A2

Titel:
KWA - REGENERATIE 1 EN 2
FLUIDA - REGENERATIE 2 (OVEN 3) MET TANKPARK 6
LEIDINGEN V/D INSTALL., INPLANTINGSPLANNEN, SCHEMA'S+LIJSTEN
PERS- EN INSTRUMENTLUCHT
PNEUMATISCH SCHEMA
LANS 2

J. Kennedylaan, 51
9042 Gent
ArcelorMittal

Plannummer: R.26981
Fase: Definitief
Folio: 0000
Discipline: 9 Pneu

10cm
ACAD